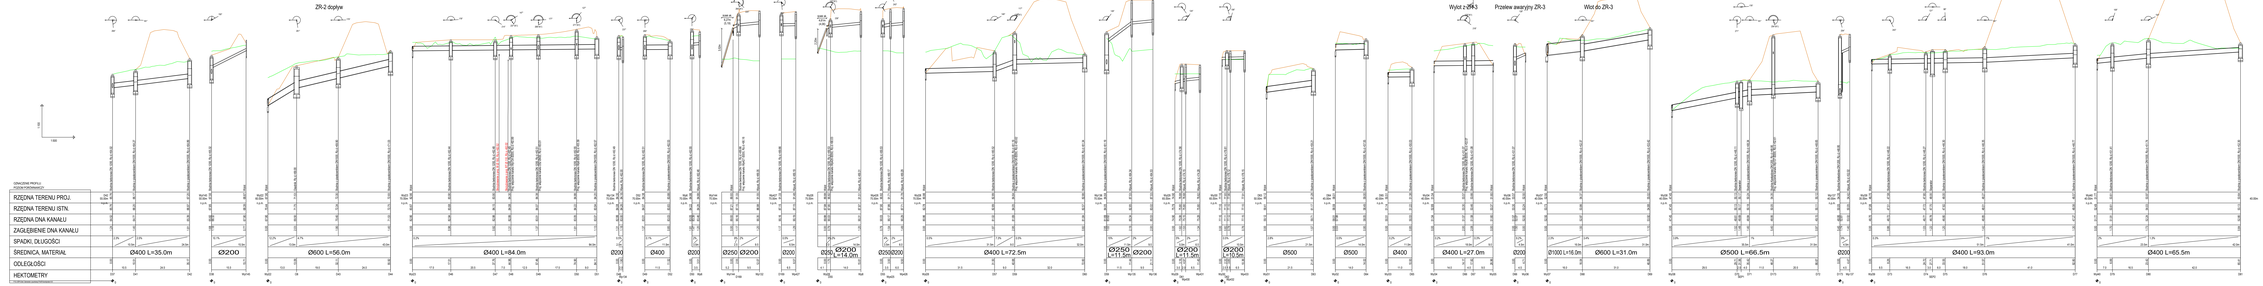

1:100
1:500
JD-2
Wlot do ZB-1a
Wylot ZB1a
Przelew ZB-1a
ZR-2 odpływ
OZNACZENIE PROFILU: Wyl1
POZIOM PORÓWNAWCZY 30.00 m n.p.m.
RZĘDNA TERENU PROJ.
RZĘDNA TERENU ISTN.
RZĘDNA DNA KANAŁU
ZAGŁĘBIENIE DNA KANAŁU
SPADKI, DŁUGOŚCI
ŚREDNICA, MATERIAŁ
ODLEGŁOŚCI
HEKTOMETRY
Ø400 L=24.0m
Ø200
Ø600 L=21.5m
Ø600 L=25.5m
Ø600 L=39.0m
Ø400 L=12.5m
Ø200
Ø500
Ø500 L=78.5m
Ø200 L=21.0m
Ø200
Ø200
Ø200
Ø200
Ø400
Ø500 L=38.0m
Ø600 L=70.0m
Ø300 L=31.5m
Ø200 L=16.0m
Ø500 L=37.0m
Ø200
Ø400 L=39.0m
Ø400 L=34.0m
Ø250
Ø200
Ø400 L=28.0m
Ø400 L=59.5m
Ø400 L=52.5m
Ø400 L=108.5m
P.S.I.EPI-Graf, Generator typunkowy Profil Koordynator 8.0

Oznaczenia:

🟩	Teren istniejący
🟧	Teren projektowany

Inwestor:

GDDKiA

Skarb Państwa - Generalny Dyrektor Dróg Krajowych i Autostrad z siedzibą w Warszawie ul. Wronia 53, 00-874 Warszawa
reprezentowany przez GDDKiA Oddział w Zielonej Górze
ul. Boh. Westerplatte 31, 65-950 Zielona Góra

Wykonawca:

POLAQUA Sp.z.o.o.
05-500 Piaseczno,
Wólka Kozodawska ul. Dworcowa 1

Jednostka projektowa:

Highway Sp. z o.o.
80-175 Gdańsk, ul. Jabłoniowa 20
tel./fax. 58 710 05 93
biuro@hwy.com.pl www.hwy.com.pl

Zadanie:

"Budowa obwodnicy miejscowości Krosno Odrzańskie w ciągu drogi krajowej nr 29"

Stadium:	PROJEKT WYKONAWCZY			
Treść rysunku:	Profile kanalizacji deszczowej			
Główny projektant:	mgr inż. Piotr Urbański	Specjalność: Drogowa Nr uprawnień: POM/0173/POOD/06	Podpis:	
Projektant:	mgr inż. Mariusz Burakowski	Specjalność: Sanitarna Nr uprawnień: Bi/194/01	Podpis:	
Projektant:	mgr inż. Aleksandra Koelmer	Specjalność: Sanitarna Nr uprawnień: POM/0463/PWBS/21	Podpis:	
Sprawdzający:	mgr inż. Agnieszka Gricman	Specjalność: Sanitarna Nr uprawnień: WAM/0082/PBS/20	Podpis:	
Opracowujący:	mgr inż. Piotr Wernecki	Specjalność: - Nr uprawnień: -	Podpis:	
Opracowujący:	inż. Marta Przysowa	Specjalność: - Nr uprawnień: -	Podpis:	

Data:	Branża:	Skala:	Rewizja:	Rysunek:
Kwiecień 2026 r.	SANITARNA	1:100/1:500	03-K00	3.1

ZR-2 dopływ
Wylot z ZR-3
Przelew awaryjny ZR-3
Wlot do ZR-3
1:100
1:500
OZNACZENIE PROFILU:
POZIOM PORÓWNAWCZY
RZĘDNA TERENU PROJ.
RZĘDNA TERENU ISTN.
RZĘDNA DNA KANAŁU
ZAGŁĘBIENIE DNA KANAŁU
SPADKI, DŁUGOŚCI
ŚREDNICA, MATERIAŁ
ODLEGŁOŚCI
HEKTOMETRY
Ø400 L=35.0m
Ø200
Ø600 L=56.0m
Ø400 L=84.0m
Ø200
Ø400
Ø200
Ø250
Ø200
Ø200
Ø250
Ø200 L=14.0m
Ø250
Ø200
Ø400 L=72.5m
Ø250 L=11.5m
Ø200
Ø200 L=11.5m
Ø200 L=10.5m
Ø500
Ø500
Ø400
Ø400 L=27.0m
Ø200
Ø1000 L=16.0m
Ø600 L=31.0m
Ø500 L=66.5m
Ø200
Ø400 L=93.0m
Ø400 L=65.5m
D37
D41
D42
D38
Wyl145
Wyl22
O8
D43
D44
Wyl23
D46
D47
D48
D49
D50
D51
Wp134
D52
Wp6
Wyl144
D169
Wp132
Wp427
Wyl26
D55
Wp8
Wp425
Wp426
Wyl28
D57
D59
D60
Wp135
Wp136
Wyl29
D61
Wp430
Wp431
Wyl30
D62
Wp432
Wp433
Wyl31
D63
Wyl32
D64
Wyl33
D65
Wyl34
D66
D67
Wyl35
Wyl36
Wyl37
D68
D69
Wyl38
D70
SEP1
D71
D173
D72
Wp137
Wyl39
D73
D74
SEP2
D75
D76
D77
Wyl40
D79
D80
D81

Oznaczenia:

🟩	Teren istniejący
🟧	Teren projektowany

Inwestor:
Skarb Państwa - Generalny Dyrektor Dróg Krajowych i Autostrad z siedzibą w Warszawie ul. Wronia 53, 00-874 Warszawa reprezentowany przez GDDKiA Oddział w Zielonej Górze ul. Boh. Westerplatte 31, 65-950 Zielona Góra

Wykonawca:
POLAQUA Sp.z.o.o.
05-500 Piaseczno,
Wólka Kozodawska ul. Dworcowa 1

Jednostka projektowa:
Highway Sp. z o.o.
80-175 Gdańsk, ul. Jabłoniowa 20
tel./fax. 58 710 05 93
biuro@hwy.com.pl www.hwy.com.pl

Zadanie:
"Budowa obwodnicy miejscowości Krosno Odrzańskie w ciągu drogi krajowej nr 29"

Stadium:	PROJEKT WYKONAWCZY		
Treść rysunku:	Profile kanalizacji deszczowej		
Główny projektant:	mgr inż. Piotr Urbański	Specjalność: Drogowa Nr uprawnień: POM/0173/POOD/06	Podpis:
Projektant:	mgr inż. Mariusz Burakowski	Specjalność: Sanitarna Nr uprawnień: BI/194/01	Podpis:
Projektant:	mgr inż. Aleksandra Koelmer	Specjalność: Sanitarna Nr uprawnień: POM/0463/PWBS/21	Podpis:
Sprawdzający:	mgr inż. Agnieszka Gricman	Specjalność: Sanitarna Nr uprawnień: WAM/0082/PBS/20	Podpis:
Opracowujący:	mgr inż. Piotr Wernecki	Specjalność: - Nr uprawnień: -	Podpis:
Opracowujący:	inż. Marta Przysowa	Specjalność: - Nr uprawnień: -	Podpis:

Data:	Branża:	Skala:	Rewizja:	Rysunek:
Kwiecień 2026 r.	SANITARNA	1:100/1:500	03-K00	3.2

1:100
1:500
OZNACZENIE PROFILU:
POZIOM PORÓWNAWCZY
RZĘDNA TERENU PROJ.
RZĘDNA TERENU ISTN.
RZĘDNA DNA KANAŁU
ZAGŁĘBIENIE DNA KANAŁU
SPADKI, DŁUGOŚCI
ŚREDNICA, MATERIAŁ
ODLEGŁOŚCI
HEKTOMETRY
Ø500 L=62.5m
Ø400
Ø400 L=36.5m
Ø200
Ø400 L=39.0m
Ø500
Ø200 L=9.0m
Ø500 L=168.0m
Ø500 L=175.0m
Ø400 L=16.5m
Ø250
Ø200 L=11.5m
Ø400 L=42.5m
Ø600 L=19.5m
Ø500 L=100.5m
Ø300 L=20.0m
Ø200 L=11.0m
Ø300 L=11.5m
Ø200 L=11.0m
Wyl41
D82
D83
D84
Wyl42
D85
Wyl43
D86
Wyl44
SEP1a
D87.2
D87
D88
Wp9
Wp10
Wyl45
SEP2a
D89
D90
D91
Wp12
Wp11
Wyl46
D92
Wyl47
D93
Wyl48
D94
Wp13
Wyl49
D95
Wp14
Wyl50
D168
SEP3
D97
D98
D99
D100
Wp138
Wp139
Wyl51
D101
D102
SEP4
D103
D104
D105
D106
D107
Wyl52
D108
D109
Wp15
Wp16
Wyl53
D110
SEP5
D111
D112
D113
Wyl54
SEP6
O10
D114
D115
D116
D117.1
D117
Wp17
D118
Wp18
Wp141
Wp19

Oznaczenia:
- Teren istniejący
- Teren projektowany

Inwestor:	GDDKiA	Skarb Państwa - Generalny Dyrektor Dróg Krajowych i Autostrad z siedzibą w Warszawie ul. Wronia 53, 00-874 Warszawa reprezentowany przez GDDKiA Oddział w Zielonej Górze ul. Boh. Westerplatte 31, 65-950 Zielona Góra
Wykonawca:	POLAQUA	POLAQUA Sp.z.o.o. 05-500 Piaseczno, Wólka Kozodawska ul. Dworcowa 1
Jednostka projektowa:	Highway	Highway Sp. z o.o. 80-175 Gdańsk, ul. Jabłoniowa 20 tel./fax. 58 710 05 93 biuro@hwy.com.pl www.hwy.com.pl

Zadanie:

"Budowa obwodnicy miejscowości Krosno Odrzańskie w ciągu drogi krajowej nr 29"

Stadium:	PROJEKT WYKONAWCZY		
Treść rysunku:	Profile kanalizacji deszczowej		
Główny projektant:	mgr inż. Piotr Urbański	Specjalność: Drogowa Nr uprawnień: POM/0173/POOD/06	Podpis:
Projektant:	mgr inż. Mariusz Burakowski	Specjalność: Sanitarna Nr uprawnień: Bł/194/01	Podpis:
Projektant:	mgr inż. Aleksandra Koelmer	Specjalność: Sanitarna Nr uprawnień: POM/0463/PWBS/21	Podpis:
Sprawdzający:	mgr inż. Agnieszka Gricman	Specjalność: Sanitarna Nr uprawnień: WAM/0082/PBS/20	Podpis:
Opracowujący:	mgr inż. Piotr Wernecki	Specjalność: - Nr uprawnień: -	Podpis:
Opracowujący:	inż. Marta Przysowa	Specjalność: - Nr uprawnień: -	Podpis:

Data:	Branża:	Skala:	Rewizja:	Rysunek:
Kwiecień 2026 r.	SANITARNA	1:100/1:500	03-K00	3.3

OZNACZENIE PROFILU:
POZIOM PORÓWNAWCZY
RZĘDNA TERENU PROJ.
RZĘDNA TERENU ISTN.
RZĘDNA DNA KANAŁU
ZAGŁĘBIENIE DNA KANAŁU
SPADKI, DŁUGOŚCI
ŚREDNICA, MATERIAŁ
ODLEGŁOŚCI
HEKTOMETRY
Ø600 L=16.0m
Ø500 L=24.0m
Ø400 L=43.0m
Ø400 L=36.0m
Ø400 L=87.0m
Ø300 L=60.0m
Ø400 L=36.5m
Ø200
Ø400 L=35.5m
Ø400
Ø300
Ø400 L=28.5m
Ø200
Ø400
Ø400 L=32.5m
Ø200
Ø200 L=13.0m
Ø400 L=38.0m
Ø250 L=13.5m
Ø200
Ø250 L=24.47m
Ø200
Ø200
Ø250
Ø200
Ø250 L=3.78m
Ø200
Ø250 L=4.07m
Ø200
Wyl57
D122
D123
Wyl58
D124
D125
D126
Wyl59
D127
Wp461
Wyl60
D128
D129
D131
D132
Wyl61
K1
O1
D133
Wyl62
Wyl63
O11
D167
D134
D135
Wp20
Wyl64
D136
D137
D138
Wyl65
D139
Wyl66
D140
D141
D142
Wyl67
D143
Wyl68
O12
D144
Wyl69
D145
Wp436
Wp437
Wyl71
D147
D165
D147.1
Wp434
Wp435
Wyl80
D149
D150
Wp428
Wp429
Wp28
Wp29
Wyl81
Wp30
Wp31
Wyl82
Wp32
Wp33
Wyl83
Wp34
Wp35
ściek sk.
11,42m
(7,36)
8,73m
12,59m
(7,10)
10,40m
11,36m
(7,04)
8,92m
10,91m
(7,98)
7,44m
P.S.I./EPI-Graf, Generator rysunkowy Profili Koordynator 8.0

Oznaczenia:

🟩 Teren istniejący

🟧 Teren projektowany

Inwestor:

GDDKiA

Skarb Państwa - Generalny Dyrektor Dróg Krajowych i Autostrad z siedzibą w Warszawie ul. Wronia 53, 00-874 Warszawa reprezentowany przez GDDKiA Oddział w Zielonej Górze ul. Boh. Westerplatte 31, 65-950 Zielona Góra

Wykonawca:

POLAQUA Sp.z.o.o.
05-500 Piaseczno,
Wólka Kozodawska ul. Dworcowa 1

Jednostka projektowa:

Highway Sp. z o.o.
80-175 Gdańsk, ul. Jabłoniowa 20
tel./fax. 58 710 05 93
biuro@hwy.com.pl www.hwy.com.pl

Zadanie:

"Budowa obwodnicy miejscowości Krosno Odrzańskie w ciągu drogi krajowej nr 29"

Stadium:	PROJEKT WYKONAWCZY		
Treść rysunku:	Profile kanalizacji deszczowej		
Główny projektant:	mgr inż. Piotr Urbański	Specjalność: Drogowa Nr uprawnień: POM/0173/POOD/06	Podpis:
Projektant:	mgr inż. Mariusz Burakowski	Specjalność: Sanitarna Nr uprawnień: Bl/194/01	Podpis:
Projektant:	mgr inż. Aleksandra Koelmer	Specjalność: Sanitarna Nr uprawnień: POM/0463/PWBS/21	Podpis:
Sprawdzający:	mgr inż. Agnieszka Gricman	Specjalność: Sanitarna Nr uprawnień: WAM/0082/PBS/20	Podpis:
Opracowujący:	mgr inż. Piotr Wernecki	Specjalność: - Nr uprawnień: -	Podpis:
Opracowujący:	inż. Marta Przysowa	Specjalność: - Nr uprawnień: -	Podpis:

Data:	Branża:	Skala:	Rewizja:	Rysunek:
Kwiecień 2026 r.	SANITARNA	1:100/1:500	03-K00	3.4

93°(87°)
212°(32°)
203°(23°)
151°(29°)
269°(89°)
182°(2°)
181°(1°)
181°(3°)
181°(2°)
178°(3°)
1:100
1:500
Proj. połączenie z przewodem Ø250 PE, Rz.o.=82.69
Skrzyżowanie z proj. KD sieci Ø300, Rz.d.=81.00
Skrzyżowanie z proj. KD sieci Ø300, Rz.d.=84.87

Oznaczenia:

- 🟩 Teren istniejący
- 🟧 Teren projektowany

OZNACZENIE PROFILU: KT1

POZIOM PORÓWNAWCZY 75.00 m n.p.m.

RZĘDNA TERENU PROJ.	84.19		84.20		83.58		83.26		83.40		83.62		83.82		84.28
RZĘDNA TERENU ISTN.	84.19		84.20		83.58		83.26		83.40		83.62		83.82		84.50
RZĘDNA OSI PRZEWODU	82.69		82.28		82.08		81.76		81.90		81.74		81.74		82.50
ZAGŁĘBIENIE OSI PRZEWODU	1.50		1.92		1.50		1.50		1.50		1.88		2.08		1.78
SPADKI, DŁUGOŚCI		2% 20.75m		0.67% 29.17m		0.49% 64.93m		0.45% 31.12m		2% 7.94		0% 7.97		2% 37.81m	
ŚREDNICA, MATERIAŁ															
ODLEGŁOŚCI	0.00	20.75	20.75	29.17	49.92	64.93	114.85	31.12	145.98	7.94	153.92	7.97	161.89	37.81	199.70
HEKTOMETRY	KT1 0		KT2		KT3	1	KT4		KT5		KT6		KT7		KT8 2

RZĘDNA TERENU PROJ.		84.83		84.64		84.99		84.99		86.50		87.62		86.03
RZĘDNA TERENU ISTN.		84.89		84.49		84.87		85.05		86.50		87.62		86.03
RZĘDNA OSI PRZEWODU		83.33		83.14		83.49		83.49		85.00		86.12		85.00
ZAGŁĘBIENIE OSI PRZEWODU		1.50		1.50		1.50		1.50		1.50		1.50		1.03
SPADKI, DŁUGOŚCI	1.12% 74.30m		0.67% 28.06m		0.57% 60.82m		0% 64.18m		4.34% 34.94m		1.4% 79.96m		0.81% 137.79m	
ŚREDNICA, MATERIAŁ					Ø250 PE L=679.75m									
ODLEGŁOŚCI	74.30	274.00	28.06	302.06	60.82	362.87	64.18	427.05	34.94	462.00	79.96	541.95	137.79	679.75
HEKTOMETRY		KT9		KT10 3		KT11	4	KT12		KT13	5	KT14	6	KT15=D139

P.S.I./EPI-Graf, Generator rysunkowy Profil Koordynator 8.0

Inwestor:

GDDKiA

Skarb Państwa - Generalny Dyrektor Dróg Krajowych i Autostrad z siedzibą w Warszawie ul. Wronia 53, 00-874 Warszawa
reprezentowany przez GDDKiA Oddział w Zielonej Górze
ul. Boh. Westerplatte 31, 65-950 Zielona Góra

Wykonawca:

POLAQUA Sp.z.o.o.
05-500 Piaseczno,
Wólka Kozodawska ul. Dworcowa 1

Jednostka projektowa:

Highway Sp. z o.o.
80-175 Gdańsk, ul. Jabłoniowa 20
tel./fax. 58 710 05 93
biuro@hwy.com.pl www.hwy.com.pl

Zadanie:

"Budowa obwodnicy miejscowości Krosno Odrzańskie w ciągu drogi krajowej nr 29"

Stadium: PROJEKT WYKONAWCZY

Treść rysunku: Profile kanalizacji deszczowej

Główny projektant:	mgr inż. Piotr Urbański	Specjalność: Drogowa Nr uprawnień: POM/0173/POOD/06	Podpis:
Projektant:	mgr inż. Mariusz Burakowski	Specjalność: Sanitarna Nr uprawnień: Bl/194/01	Podpis:
Projektant:	mgr inż. Aleksandra Koelmer	Specjalność: Sanitarna Nr uprawnień: POM/0463/PWBS/21	Podpis:
Sprawdzający:	mgr inż. Agnieszka Gricman	Specjalność: Sanitarna Nr uprawnień: WAM/0082/PBS/20	Podpis:
Opracowujący:	mgr inż. Piotr Wernecki	Specjalność: - Nr uprawnień: -	Podpis:
Opracowujący:	inż. Marta Przysowa	Specjalność: - Nr uprawnień: -	Podpis:

Data:	Branża:	Skala:	Rewizja:	Rysunek:
Kwiecień 2026 r.	SANITARNA	1:100/1:500	03-K00	3.5

OZNACZENIE PROFILU:
POZIOM PORÓWNAWCZY
RZĘDNA TERENU PROJ.
RZĘDNA TERENU ISTN.
RZĘDNA DNA KANAŁU
ZAGŁĘBIENIE DNA KANAŁU
SPADKI, DŁUGOŚCI
ŚREDNICA, MATERIAŁ
ODLEGŁOŚCI
HEKTOMETRY
P.S.I./EPI-Graf, Generator rysunkowy Profili Koordynator 8.0
Wyl84 30.00m n.p.m. | ściek sk. 6,38m (4,13) | 4,87m | Wylot | Wpust, Rz.d.=45.27 | Wpust, Rz.d.=45.46 | 46.04 47.66 47.66 | 41.05 41.04 40.84 | 46.04 46.27 46.46 | 0.00 1.39 1.20 | 9% 2.6 | 2% 9.7 | Ø250 Ø200 | 0.00 2.56 12.28 | 4.1 9.7 | Wyl84 Wp36 Wp37 | 0
Wyl85 30.00m n.p.m. | ściek sk. 5,61m (3,68) | 4,23m | Wylot | Wpust, Rz.d.=44.58 | Wpust, Rz.d.=44.77 | 45.34 46.97 46.97 | 40.75 40.93 41.33 | 45.34 45.58 45.77 | 0.00 1.39 1.20 | 9% 2.6 | 2% 9.7 | Ø250 Ø200 | 0.00 2.59 12.31 | 3.7 9.7 | Wyl85 Wp38 Wp39 | 0
Wyl86 30.00m n.p.m. | 181° | ściek sk. 4,82m (3,04) | 3,74m | Wylot | Wpust, Rz.d.=44.02 | Wpust, Rz.d.=44.21 | 44.79 46.41 46.41 | 41.08 41.27 40.88 | 44.79 45.02 45.21 | 0.00 1.39 1.20 | 9% 2.5 | 2% 9.7 | Ø250 Ø200 | 0.00 2.48 12.21 | 3.0 9.7 | Wyl86 Wp40 Wp41 | 0
Wyl87 30.00m n.p.m. | ściek sk. 4,22m (2,54) | 3,37m | Wylot | Wpust, Rz.d.=43.58 | Wpust, Rz.d.=43.77 | 44.36 45.98 45.97 | 40.77 40.61 40.54 | 44.36 44.58 44.77 | 0.00 1.40 1.20 | 9% 2.4 | 2% 9.7 | Ø250 Ø200 | 0.00 2.39 12.11 | 2.5 9.7 | Wyl87 Wp42 Wp43 | 0
Wyl88 30.00m n.p.m. | ściek sk. 3,79m (2,12) | 3,14m | Wylot | Wpust, Rz.d.=43.28 | Wpust, Rz.d.=43.47 | 44.07 45.67 45.67 | 40.59 40.59 40.68 | 44.07 44.28 44.47 | 0.00 1.39 1.20 | 9% 2.3 | 2% 9.7 | Ø250 Ø200 | 0.00 2.26 11.98 | 2.1 9.7 | Wyl88 Wp44 Wp45 | 0
Wyl89 30.00m n.p.m. | ściek sk. 4,00m (2,66) | 2,99m | Wylot | Wpust, Rz.d.=43.10 | Wpust, Rz.d.=43.29 | 43.86 45.49 45.49 | 40.62 40.23 40.50 | 43.86 44.10 44.29 | 0.00 1.39 1.20 | 9% 2.6 | 2% 9.7 | Ø250 Ø200 | 0.00 2.63 12.35 | 2.7 9.7 | Wyl89 Wp46 Wp47 | 0
Wyl90 30.00m n.p.m. | ściek sk. 4,04m (2,46) | 3,21m | Wylot | Wpust, Rz.d.=43.17 | Wpust, Rz.d.=43.36 | 43.95 45.56 45.56 | 40.81 40.78 40.44 | 43.95 44.17 44.36 | 0.00 1.39 1.20 | 9% 2.4 | 2% 9.7 | Ø250 Ø200 | 0.00 2.41 12.13 | 2.5 9.7 | Wyl90 Wp48 Wp49 | 0
Wyl91 30.00m n.p.m. | ściek sk. 3,76m (1,72) | 3,34m | Wylot | Wpust, Rz.d.=43.05 | Wpust, Rz.d.=43.24 | 43.86 45.44 45.44 | 40.12 40.19 40.38 | 43.86 44.05 44.24 | 0.00 1.39 1.20 | 9.3% 2.0 | 2% 9.5 | Ø250 Ø200 | 0.00 2.01 11.73 | 1.7 9.5 | Wyl91 Wp50 Wp51 | 0
Wyl92 | 179° | ściek sk. 4,48m (2,82) | 3,48m | Wylot | Wpust, Rz.d.=43.58 | 44.16 45.78 45.78 | 40.61 40.59 40.44 | 44.16 44.39 44.58 | 0.00 1.39 1.20 | 9% 2.5 | 2% 9.7 | Ø250 Ø200 | 0.00 2.49 12.21 | 2.8 9.7 | Wyl92 Wp52 Wp53 | 0
Wyl93 30.00m n.p.m. | 179° | ściek sk. 4,23m (2,06) | 3,70m | Wylot | Wpust, Rz.d.=43.66 | Wpust, Rz.d.=43.85 | 44.32 46.05 46.05 | 40.43 40.38 40.12 | 44.32 44.66 44.85 | 0.00 1.39 1.20 | 9% 3.8 | 2% 9.7 | Ø250 Ø200 | 0.00 3.77 13.49 | 2.1 9.7 | Wyl93 Wp54 Wp55 | 0
Wyl94 30.00m n.p.m. | ściek sk. 5,30m (3,39) | 4,07m | Wylot | Wpust, Rz.d.=43.93 | Wpust, Rz.d.=44.12 | 44.70 46.32 46.32 | 40.30 40.42 40.24 | 44.70 44.93 45.12 | 0.00 1.39 1.20 | 9% 2.5 | 2% 9.7 | Ø250 Ø200 | 0.00 2.52 12.24 | 3.4 9.7 | Wyl94 Wp56 Wp57 | 0
Wyl95 30.00m n.p.m. | ściek sk. 5,30m (2,91) | 4,42m | Wylot | Wpust, Rz.d.=44.20 | Wpust, Rz.d.=44.39 | 44.99 46.59 46.59 | 40.28 40.20 39.78 | 44.99 45.20 45.39 | 0.00 1.39 1.20 | 9% 2.2 | 2% 9.7 | Ø250 Ø200 | 0.00 2.25 11.97 | 2.9 9.7 | Wyl95 Wp58 Wp59 | 0
Wyl96 30.00m n.p.m. | 182° | ściek sk. 5,51m (2,99) | 4,64m | Wylot | Wpust, Rz.d.=44.46 | Wpust, Rz.d.=44.65 | 45.15 46.85 46.85 | 40.16 40.04 39.96 | 45.15 45.46 45.65 | 0.00 1.39 1.20 | 9% 3.4 | 2% 9.7 | Ø250 Ø200 | 0.00 3.44 13.17 | 3.0 9.7 | Wyl96 Wp60 Wp61 | 0
Wyl97 30.00m n.p.m. | 223° | 104° | 185° | 263° | Wylot | Studnia betonowa DN 1200, Rz.d.=39.02 | Studnia betonowa DN 1200, Rz.d.=39.09 | Separator | Studnia z piaskownikiem DN1500, Rz.d.=39.12 | Studnia z piaskownikiem DN1500, Rz.d.=39.36 | 39.40 40.70 40.70 40.70 40.83 40.79 | 39.62 39.63 39.79 39.97 40.14 40.19 | 39.50 39.52 39.59 39.60 39.62 39.86 | -0.10 1.18 1.11 1.10 1.21 0.93 | 0.4% 29.5m | 2% 12.0m | Ø400 L=42.0m | 0.00 3.88 21.72 24.57 29.77 41.89 | 0.3 18.0 3.0 5.0 12.0 | Wyl97 D164 D151 SEP4a D153 D154 | 0
Wp63 70.00m n.p.m. | Wylot | Wpust, Rz.d.=82.23 | 83.19 84.29 | 83.53 84.58 | 83.19 83.23 | 0.00 1.06 | 0.5% 8.5 | Ø200 | 0.00 8.74 | 0.1 | Wyl99 Wp63 | 0
Wp64 70.00m n.p.m. | Wylot | Wpust, Rz.d.=81.35 | 81.87 83.75 | 82.14 83.27 | 81.97 82.35 | -0.10 1.40 | 3.8% 10.0m | Ø200 | 0.00 10.11 | 0.1 | Wyl100 Wp64 | 0
D155 70.00m n.p.m. | Wylot | Studnia z piaskownikiem DN1500, Rz.d.=82.26 | 82.70 83.81 | 83.57 83.64 | 82.70 82.76 | 0.00 1.05 | 0.3% 20.5m | Ø500 | 0.00 20.31 | 20.5 | Wyl101 D155 | 0
Wp65 70.00m n.p.m. | Wylot | Wpust, Rz.d.=82.12 | 82.77 84.19 | 83.65 83.74 | 83.07 83.12 | -0.30 1.07 | 0.5% 9.6 | Ø200 | 0.00 9.89 | 0.3 | Wyl102 Wp65 | 0
Wp66 70.00m n.p.m. | Wylot | Wpust, Rz.d.=82.54 | 83.44 84.47 | 83.70 83.78 | 83.50 83.54 | -0.06 0.93 | 0.5% 8.4 | Ø200 | 0.00 8.48 | 0.0 | Wyl103 Wp66 | 0
Wp67 70.00m n.p.m. | Wylot | Wpust, Rz.d.=83.03 | 83.60 85.01 | 84.59 84.70 | 84.00 84.03 | -0.40 0.98 | 0.5% 6.4 | Ø200 | 0.00 6.65 | 0.3 | Wyl104 Wp67 | 0
Wp68 75.00m n.p.m. | Wylot | Wpust, Rz.d.=83.55 | 84.37 85.38 | 85.19 85.33 | 84.50 84.55 | -0.13 0.83 | 0.5% 9.5 | Ø200 | 0.00 9.58 | 0.1 | Wyl105 Wp68 | 0
Wp69 75.00m n.p.m. | Wylot | Wpust, Rz.d.=83.54 | 84.31 85.67 | 85.28 85.43 | 84.51 84.54 | -0.20 1.13 | 0.5% 6.3 | Ø200 | 0.00 6.61 | 0.3 | Wyl106 Wp69 | 0
Wp70 75.00m n.p.m. | Wylot | Wpust, Rz.d.=83.84 | 84.57 85.76 | 85.57 85.57 | 84.80 84.84 | -0.23 0.92 | 0.5% 7.5 | Ø200 | 0.00 7.79 | 0.3 | Wyl107 Wp70 | 0
Wp71 75.00m n.p.m. | Wylot | Wpust, Rz.d.=83.38 | 84.12 85.45 | 85.50 85.52 | 84.32 84.38 | -0.20 1.07 | 0.5% 11.5m | Ø200 | 0.00 11.73 | 0.2 | Wyl108 Wp71 | 0
Wyl109 30.00m n.p.m. | 119° | 249° | ściek sk. 5,34m (4,44) | 2,96m | Wylot | Studnia betonowa DN 1200, Rz.d.=47.54 | Wpust, Rz.d.=48.13 | Wpust, Rz.d.=48.32 | 47.41 51.04 50.99 50.99 | 43.82 43.90 43.86 43.72 | 47.41 48.04 49.09 49.13 49.32 | 0.00 3.00 1.95 1.86 1.67 | 9% 7.0 | 2% 11.5m | Ø250 Ø200 | 0.00 6.99 8.73 18.46 | 4.4 1.7 9.7 | Wyl109 D156 Wp72 Wp73 | 0
Wyl110 30.00m n.p.m. | ściek sk. 6,49m (5,39) | 3,62m | Wylot | Wpust, Rz.d.=47.44 | Wpust, Rz.d.=47.63 | 47.99 49.83 49.83 | 41.01 41.16 41.80 | 47.99 48.44 48.63 | 0.00 1.39 1.20 | 9% 5.0 | 2% 9.7 | Ø250 Ø200 | 0.00 4.96 14.67 | 5.4 9.7 | Wyl110 Wp74 Wp75 | 0
Wyl111 30.00m n.p.m. | ściek sk. 5,01m (4,15) | 2,80m | Wylot | Wpust, Rz.d.=46.45 | Wpust, Rz.d.=46.64 | 47.11 48.83 48.84 | 40.62 40.66 40.57 | 47.11 47.45 47.64 | 0.00 1.38 1.20 | 9% 3.7 | 2% 9.7 | Ø250 Ø200 | 0.00 3.73 13.44 | 4.2 9.7 | Wyl111 Wp76 Wp77 | 0
Wyl113 30.00m n.p.m. | 178° | ściek sk. 3,50m (2,90) | 1,96m | Wylot | Wpust, Rz.d.=45.55 | Wpust, Rz.d.=45.74 | 46.21 47.94 47.94 | 40.46 40.58 40.68 | 46.21 46.55 46.74 | 0.00 1.39 1.20 | 9% 3.8 | 2% 9.5 | Ø250 Ø200 | 0.00 3.81 13.35 | 2.9 9.5 | Wyl113 Wp78 Wp79 | 0
Wyl114 30.00m n.p.m. | ściek sk. 2,20m (1,82) | 1,23m | Wylot | Wpust, Rz.d.=44.76 | Wpust, Rz.d.=44.95 | 45.42 47.15 47.15 | 40.91 40.93 40.90 | 45.42 45.76 45.95 | 0.00 1.39 1.20 | 9% 3.7 | 2% 9.7 | Ø250 Ø200 | 0.00 3.69 13.41 | 1.8 9.7 | Wyl114 Wp80 Wp81 | 0
Wyl115 30.00m n.p.m. | 182° | ściek sk. 1,06m (0,88) | 0,60m | Wylot | Wpust, Rz.d.=44.06 | Wpust, Rz.d.=44.25 | 44.79 46.45 46.45 | 41.09 41.15 41.46 | 44.79 45.06 45.25 | 0.00 1.39 1.20 | 9% 3.7 | 2% 9.5 | Ø250 Ø200 | 0.00 3.70 13.25 | 0.9 9.5 | Wyl115 Wp82 Wp83 | 0
Wyl116 30.00m n.p.m. | 179.3° | Wylot | Wpust, Rz.d.=43.47 | Wpust, Rz.d.=43.66 | 44.13 45.85 45.86 | 40.71 40.72 40.75 | 44.13 44.47 44.66 | 0.00 1.38 1.20 | 9% 3.8 | 2% 9.5 | Ø250 Ø200 | 0.00 3.76 13.31 | 0.1 9.5 | Wyl116 Wp84 Wp85 | 0
Wyl117 30.00m n.p.m. | ściek sk. 0,19m (0,08) | 0,17m | Wylot | Wpust, Rz.d.=42.97 | Wpust, Rz.d.=43.16 | 43.88 45.36 45.36 | 40.71 40.71 40.68 | 43.88 43.97 44.16 | 0.00 1.39 1.20 | 2.8% 3.0 | 2% 9.6 | Ø250 Ø200 | 0.00 3.04 12.67 | 0.1 9.6 | Wyl117 Wp86 Wp87 | 0
Wyl118 30.00m n.p.m. | 180.5° | ściek sk. 0,29m (0,21) | 0,20m | Wylot | Wpust, Rz.d.=42.86 | Wpust, Rz.d.=42.91 | 43.85 44.96 44.96 | 40.63 40.63 40.63 | 43.85 43.86 43.91 | 0.00 1.10 1.05 | 0.5% 12.1m | Ø250 Ø200 | 0.00 2.38 12.10 | 0.2 9.7 | Wyl118 Wp88 Wp89 | 0
Wyl119 30.00m n.p.m. | ściek sk. 0,28m (0,19) | 0,20m | Wylot | Wpust, Rz.d.=42.80 | Wpust, Rz.d.=42.85 | 43.79 44.67 44.67 | 40.62 40.62 40.68 | 43.79 43.80 43.85 | 0.00 0.87 0.82 | 0.5% 11.8m | Ø250 Ø200 | 0.00 2.05 11.77 | 0.2 9.7 | Wyl119 Wp90 Wp91 | 0
Wyl120 30.00m n.p.m. | 178.7° | Wylot | Wpust, Rz.d.=42.59 | Wpust, Rz.d.=42.64 | 43.55 44.47 44.47 | 40.69 40.65 40.68 | 43.58 43.59 43.64 | -0.03 0.88 0.83 | 0.5% 11.8m | Ø250 Ø200 | 0.00 2.11 11.80 | 0.0 9.7 | Wyl120 Wp92 Wp93 | 0

Oznaczenia:

🟩	Teren istniejący
🟧	Teren projektowany

Inwestor: GDDKiA
Skarb Państwa - Generalny Dyrektor Dróg Krajowych i Autostrad z siedzibą w Warszawie ul. Wronia 53, 00-874 Warszawa
reprezentowany przez GDDKiA Oddział w Zielonej Górze
ul. Boh. Westerplatte 31, 65-950 Zielona Góra

Wykonawca: POLAQUA
POLAQUA Sp.z.o.o.
05-500 Piaseczno,
Wólka Kozodawska ul. Dworcowa 1

Jednostka projektowa: Highway
Highway Sp. z o.o.
80-175 Gdańsk, ul. Jabłoniowa 20
tel./fax. 58 710 05 93
biuro@hwy.com.pl www.hwy.com.pl

Zadanie:
"Budowa obwodnicy miejscowości Krosno Odrzańskie w ciągu drogi krajowej nr 29"

Stadium: PROJEKT WYKONAWCZY
Treść rysunku: Profile kanalizacji deszczowej

Główny projektant:	mgr inż. Piotr Urbański	Specjalność: Drogowa Nr uprawnień: POM/0173/POOD/06	Podpis:
Projektant:	mgr inż. Mariusz Burakowski	Specjalność: Sanitarna Nr uprawnień: Bł/194/01	Podpis:
Projektant:	mgr inż. Aleksandra Koelmer	Specjalność: Sanitarna Nr uprawnień: POM/0463/PWBS/21	Podpis:
Sprawdzający:	mgr inż. Agnieszka Gricman	Specjalność: Sanitarna Nr uprawnień: WAM/0082/PBS/20	Podpis:
Opracowujący:	mgr inż. Piotr Wernecki	Specjalność: - Nr uprawnień: -	Podpis:
Opracowujący:	inż. Marta Przysowa	Specjalność: - Nr uprawnień: -	Podpis:

Data:	Branża:	Skala:	Rewizja:	Rysunek:
Kwiecień 2026 r.	SANITARNA	1:100/1:500	03-K00	3.6

Oznaczenia:

🟩 Teren istniejący
🟧 Teren projektowany

OZNACZENIE PROFILU:
POZIOM PORÓWNAWCZY
RZĘDNA TERENU PROJ.
RZĘDNA TERENU ISTN.
RZĘDNA DNA KANAŁU
ZAGŁĘBIENIE DNA KANAŁU
SPADKI, DŁUGOŚCI
ŚREDNICA, MATERIAŁ
ODLEGŁOŚCI
HEKTOMETRY
P.S.I./EPI-Graf, Generator rysunkowy Profil Koordynator 8.0
Wyl121 30.00m n.p.m.
Wyl122 30.00m n.p.m.
Wyl123 30.00m n.p.m.
Wp100 30.00m n.p.m.
D158 30.00m n.p.m.
Wp101 30.00m n.p.m.
Wyl127 30.00m n.p.m.
Wyl128 30.00m n.p.m.
Wyl129 30.00m n.p.m.
Wyl130 30.00m n.p.m.
Wyl131 30.00m n.p.m.
Wyl132 30.00m n.p.m.
Wyl133 30.00m n.p.m.
Wyl135 30.00m n.p.m.
Wyl136 30.00m n.p.m.
Wyl137 30.00m n.p.m.
D159 30.00m n.p.m.
Wyl140 30.00m n.p.m.
Wp439 30.00m n.p.m.
Wp129 70.00m n.p.m.
D163 45.00m n.p.m.
Wyl142 75.00m n.p.m.
D12 70.00m n.p.m.
Wyl427 35.00m n.p.m.
Wp5 70.00m n.p.m.
Wyl446 35.00m n.p.m.
Ø250 Ø200
Ø400
Ø200 L=13.1m
Ø200 L=41.0m
ściek sk.
Studnia z piaskownikiem DN1500
Studnia betonowa DN 1200
Wpust
Wylot
Teren istniejący
Teren projektowany

Inwestor:	GDDKiA Skarb Państwa - Generalny Dyrektor Dróg Krajowych i Autostrad z siedzibą w Warszawie ul. Wronia 53, 00-874 Warszawa reprezentowany przez GDDKiA Oddział w Zielonej Górze ul. Boh. Westerplatte 31, 65-950 Zielona Góra
Wykonawca:	POLAQUA Sp.z.o.o. 05-500 Piaseczno, Wólka Kozodawska ul. Dworcowa 1
Jednostka projektowa:	Highway Sp. z o.o. 80-175 Gdańsk, ul. Jabłoniowa 20 tel./fax. 58 710 05 93 biuro@hwy.com.pl www.hwy.com.pl
Zadanie:	"Budowa obwodnicy miejscowości Krosno Odrzańskie w ciągu drogi krajowej nr 29"
Stadium:	PROJEKT WYKONAWCZY
Treść rysunku:	Profile kanalizacji deszczowej

Główny projektant:	mgr inż. Piotr Urbański	Specjalność: Drogowa Nr uprawnień: POM/0173/POOD/06	Podpis:
Projektant:	mgr inż. Mariusz Burakowski	Specjalność: Sanitarna Nr uprawnień: BI/194/01	Podpis:
Projektant:	mgr inż. Aleksandra Koelmer	Specjalność: Sanitarna Nr uprawnień: POM/0463/PWBS/21	Podpis:
Sprawdzający:	mgr inż. Agnieszka Gricman	Specjalność: Sanitarna Nr uprawnień: WAM/0082/PBS/20	Podpis:
Opracowujący:	mgr inż. Piotr Wernecki	Specjalność: - Nr uprawnień: -	Podpis:
Opracowujący:	inż. Marta Przysowa	Specjalność: - Nr uprawnień: -	Podpis:

Data:	Branża:	Skala:	Rewizja:	Rysunek:
Kwiecień 2026 r.	SANITARNA	1:100/1:500	03-K00	3.7

1:100
1:500
OZNACZENIE PROFILU: Wp250
POZIOM PORÓWNAWCZY 35.00 m n.p.m.
RZĘDNA TERENU PROJ.
RZĘDNA TERENU ISTN.
RZĘDNA DNA KANAŁU
ZAGŁĘBIENIE DNA KANAŁU
SPADKI, DŁUGOŚCI
ŚREDNICA, MATERIAŁ
ODLEGŁOŚCI
HEKTOMETRY
Wylot
Ø200
Ø200 SN 12
ściek sk.
P.S.I./EPI-Graf, Generator rysunkowy Profili Koordynator 8.0

Oznaczenia:

- Teren istniejący
- Teren projektowany

Inwestor:	GDDKiA Skarb Państwa - Generalny Dyrektor Dróg Krajowych i Autostrad z siedzibą w Warszawie ul. Wronia 53, 00-874 Warszawa reprezentowany przez GDDKiA Oddział w Zielonej Górze ul. Boh. Westerplatte 31, 65-950 Zielona Góra
Wykonawca:	POLAQUA Sp.z.o.o. 05-500 Piaseczno, Wólka Kozodawska ul. Dworcowa 1
Jednostka projektowa:	Highway Sp. z o.o. 80-175 Gdańsk, ul. Jabłoniowa 20 tel./fax. 58 710 05 93 biuro@hwy.com.pl www.hwy.com.pl
Zadanie:	"Budowa obwodnicy miejscowości Krosno Odrzańskie w ciągu drogi krajowej nr 29"
Stadium:	PROJEKT WYKONAWCZY
Treść rysunku:	Profile kanalizacji deszczowej

Główny projektant:	mgr inż. Piotr Urbański	Specjalność: Drogowa Nr uprawnień: POM/0173/POOD/06	Podpis:
Projektant:	mgr inż. Mariusz Burakowski	Specjalność: Sanitarna Nr uprawnień: BI/194/01	Podpis:
Projektant:	mgr inż. Aleksandra Koelmer	Specjalność: Sanitarna Nr uprawnień: POM/0463/PWBS/21	Podpis:
Sprawdzający:	mgr inż. Agnieszka Gricman	Specjalność: Sanitarna Nr uprawnień: WAM/0082/PBS/20	Podpis:
Opracowujący:	mgr inż. Piotr Wernecki	Specjalność: - Nr uprawnień: -	Podpis:
Opracowujący:	inż. Marta Przysowa	Specjalność: - Nr uprawnień: -	Podpis:

Data:	Branża:	Skala:	Rewizja:	Rysunek:
Kwiecień 2026 r.	SANITARNA	1:100/1:500	03-K00	3.8

OZNACZENIE PROFILU:
POZIOM PORÓWNAWCZY
RZĘDNA TERENU PROJ.
RZĘDNA TERENU ISTN.
RZĘDNA DNA KANAŁU
ZAGŁĘBIENIE DNA KANAŁU
SPADKI, DŁUGOŚCI
ŚREDNICA, MATERIAŁ
ODLEGŁOŚCI
HEKTOMETRY
P.S.I./EPI-Graf, Generator rysunkowy Profili Koordynator 8.0
ściek sk.
Wylot
Wpust
Ø200
Wp301 … Wp354
Wyl303 … Wyl356

Oznaczenia:

Teren istniejący

Teren projektowany

Inwestor:	Skarb Państwa - Generalny Dyrektor Dróg Krajowych i Autostrad z siedzibą w Warszawie ul. Wronia 53, 00-874 Warszawa reprezentowany przez GDDKiA Oddział w Zielonej Górze ul. Boh. Westerplatte 31, 65-950 Zielona Góra
Wykonawca:	POLAQUA Sp.z.o.o. 05-500 Piaseczno, Wólka Kozodawska ul. Dworcowa 1
Jednostka projektowa:	Highway Sp. z o.o. 80-175 Gdańsk, ul. Jabłoniowa 20 tel./fax. 58 710 05 93 biuro@hwy.com.pl www.hwy.com.pl
Zadanie:	"Budowa obwodnicy miejscowości Krosno Odrzańskie w ciągu drogi krajowej nr 29"
Stadium:	PROJEKT WYKONAWCZY
Treść rysunku:	Profile kanalizacji deszczowej

Główny projektant:	mgr inż. Piotr Urbański	Specjalność: Drogowa Nr uprawnień: POM/0173/POOD/06	Podpis:
Projektant:	mgr inż. Mariusz Burakowski	Specjalność: Sanitarna Nr uprawnień: Bł/194/01	Podpis:
Projektant:	mgr inż. Aleksandra Koelmer	Specjalność: Sanitarna Nr uprawnień: POM/0463/PWBS/21	Podpis:
Sprawdzający:	mgr inż. Agnieszka Gricman	Specjalność: Sanitarna Nr uprawnień: WAM/0082/PBS/20	Podpis:
Opracowujący:	mgr inż. Piotr Wernecki	Specjalność: - Nr uprawnień: -	Podpis:
Opracowujący:	inż. Marta Przysowa	Specjalność: - Nr uprawnień: -	Podpis:

Data:	Branża:	Skala:	Rewizja:	Rysunek:
Kwiecień 2026 r.	SANITARNA	1:100/1:500	03-K00	3.9

OZNACZENIE PROFILU:
POZIOM PORÓWNAWCZY
RZĘDNA TERENU PROJ.
RZĘDNA TERENU ISTN.
RZĘDNA DNA KANAŁU
ZAGŁĘBIENIE DNA KANAŁU
SPADKI, DŁUGOŚCI
ŚREDNICA, MATERIAŁ
ODLEGŁOŚCI
HEKTOMETRY
P.S.I./EPI-Graf, Generator rysunkowy Profili Koordynator 8.0
ściek sk.
Ø200
Ø200 L=41.0m
Ø200 L=42.5m
Wylot
Wpust, Rz.d.
n.p.m.
Wp355
Wp356
Wp360
Wp361
Wp362
Wp363
Wp366
Wp367
Wp368
Wp369
Wp370
Wp371
Wp372
Wp373
Wyl376
Wyl377
Wp441
Wp442
Wp376
Wp377
Wp378
Wp379
Wp380
Wp381
Wp382
Wp383
Wp384
Wp385
Wp386
Wp387
Wp388
Wp389
Wp390
Wp391
Wp392
Wp393
Wp394
Wp146
Wp147
Wp148
Wp149
Wp150
Wp151
Wp152
Wp153
Wp154
Wp155
Wp156
Wp157

Oznaczenia:

- Teren istniejący
- Teren projektowany

Inwestor:	GDDKiA Skarb Państwa - Generalny Dyrektor Dróg Krajowych i Autostrad z siedzibą w Warszawie ul. Wronia 53, 00-874 Warszawa reprezentowany przez GDDKiA Oddział w Zielonej Górze ul. Boh. Westerplatte 31, 65-950 Zielona Góra
Wykonawca:	POLAQUA POLAQUA Sp.z.o.o. 05-500 Piaseczno, Wólka Kozodawska ul. Dworcowa 1
Jednostka projektowa:	Highway Highway Sp. z o.o. 80-175 Gdańsk, ul. Jabłoniowa 20 tel./fax. 58 710 05 93 biuro@hwy.com.pl www.hwy.com.pl
Zadanie:	"Budowa obwodnicy miejscowości Krosno Odrzańskie w ciągu drogi krajowej nr 29"
Stadium:	PROJEKT WYKONAWCZY
Treść rysunku:	Profile kanalizacji deszczowej

Główny projektant:	mgr inż. Piotr Urbański	Specjalność: Drogowa Nr uprawnień: POM/0173/POOD/06	Podpis:
Projektant:	mgr inż. Mariusz Burakowski	Specjalność: Sanitarna Nr uprawnień: BI/194/01	Podpis:
Projektant:	mgr inż. Aleksandra Koelmer	Specjalność: Sanitarna Nr uprawnień: POM/0463/PWBS/21	Podpis:
Sprawdzający:	mgr inż. Agnieszka Gricman	Specjalność: Sanitarna Nr uprawnień: WAM/0082/PBS/20	Podpis:
Opracowujący:	mgr inż. Piotr Wernecki	Specjalność: - Nr uprawnień: -	Podpis:
Opracowujący:	inż. Marta Przysowa	Specjalność: - Nr uprawnień: -	Podpis:

Data:	Branża:	Skala:	Rewizja:	Rysunek:
Kwiecień 2026 r.	SANITARNA	1:100/1:500	03-K00	3.10

OZNACZENIE PROFILU:
POZIOM PORÓWNAWCZY
RZĘDNA TERENU PROJ.
RZĘDNA TERENU ISTN.
RZĘDNA DNA KANAŁU
ZAGŁĘBIENIE DNA KANAŁU
SPADKI, DŁUGOŚCI
ŚREDNICA, MATERIAŁ
ODLEGŁOŚCI
HEKTOMETRY
ściek sk.
Wylot
Wpust
Ø200
Wp159
Wp160
Wp161
Wp162
Wp163
Wp164
Wp165
Wp166
Wp167
Wp168
Wp169
Wp170
Wp171
Wp172
Wp173
Wp174
Wp175
Wp176
Wp177
Wp178
Wp179
Wp180
Wp181
Wp182
Wp183
Wp185
Wp186
Wp187
Wp188
Wp189
Wp190
Wp191
Wp192
Wp193
Wp194
Wp195
Wp196
Wp198
Wp199
Wp200
Wp201
Wp203
Wp204
Wp205
Wp206
Wp207
P.S.I. EPI-Graf, Generator rysunkowy Profil Koordynator 8.0

Oznaczenia:
- Teren istniejący
- Teren projektowany

Inwestor: Skarb Państwa - Generalny Dyrektor Dróg Krajowych i Autostrad z siedzibą w Warszawie ul. Wronia 53, 00-874 Warszawa reprezentowany przez GDDKiA Oddział w Zielonej Górze ul. Boh. Westerplatte 31, 65-950 Zielona Góra

Wykonawca: POLAQUA Sp.z.o.o.
05-500 Piaseczno,
Wólka Kozodawska ul. Dworcowa 1

Jednostka projektowa: Highway Sp. z o.o.
80-175 Gdańsk, ul. Jabłoniowa 20
tel./fax. 58 710 05 93
biuro@hwy.com.pl www.hwy.com.pl

Zadanie:

"Budowa obwodnicy miejscowości Krosno Odrzańskie w ciągu drogi krajowej nr 29"

Stadium:	PROJEKT WYKONAWCZY		
Treść rysunku:	Profile kanalizacji deszczowej		
Główny projektant:	mgr inż. Piotr Urbański	Specjalność: Drogowa Nr uprawnień: POM/0173/POOD/06	Podpis:
Projektant:	mgr inż. Mariusz Burakowski	Specjalność: Sanitarna Nr uprawnień: BI/194/01	Podpis:
Projektant:	mgr inż. Aleksandra Koelmer	Specjalność: Sanitarna Nr uprawnień: POM/0463/PWBS/21	Podpis:
Sprawdzający:	mgr inż. Agnieszka Gricman	Specjalność: Sanitarna Nr uprawnień: WAM/0082/PBS/20	Podpis:
Opracowujący:	mgr inż. Piotr Wernecki	Specjalność: - Nr uprawnień: -	Podpis:
Opracowujący:	inż. Marta Przysowa	Specjalność: - Nr uprawnień: -	Podpis:

Data:	Branża:	Skala:	Rewizja:	Rysunek:
Kwiecień 2026 r.	SANITARNA	1:100/1:500	03-K00	3.11

OZNACZENIE PROFILU:
POZIOM PORÓWNAWCZY
RZĘDNA TERENU PROJ.
RZĘDNA TERENU ISTN.
RZĘDNA DNA KANAŁU
ZAGŁĘBIENIE DNA KANAŁU
SPADKI, DŁUGOŚCI
ŚREDNICA, MATERIAŁ
ODLEGŁOŚCI
HEKTOMETRY
ściek sk.
Wylot
Wpust
Ø200
Ø400 L=30.5m
Studnia z piaskownikiem DN2000, Rz.d.=81.97
Studnia z piaskownikiem DN1500, Rz.d.=82.10
S.S.S.Ws7
S.S.S.Ws8
236°
P.S.I./EPI-Graf, Generator rysunkowy Profil Koordynator 8.0

Oznaczenia:

— Teren istniejący

— Teren projektowany

Inwestor:

Skarb Państwa - Generalny Dyrektor Dróg Krajowych i Autostrad z siedzibą w Warszawie ul. Wronia 53, 00-874 Warszawa reprezentowany przez GDDKiA Oddział w Zielonej Górze ul. Boh. Westerplatte 31, 65-950 Zielona Góra

Wykonawca:

POLAQUA Sp.z.o.o.
05-500 Piaseczno,
Wólka Kozodawska ul. Dworcowa 1

Jednostka projektowa:

Highway Sp. z o.o.
80-175 Gdańsk, ul. Jabłoniowa 20
tel./fax. 58 710 05 93
biuro@hwy.com.pl www.hwy.com.pl

Zadanie:

"Budowa obwodnicy miejscowości Krosno Odrzańskie w ciągu drogi krajowej nr 29"

Stadium:	PROJEKT WYKONAWCZY		
Treść rysunku:	Profile kanalizacji deszczowej		
Główny projektant:	mgr inż. Piotr Urbański	Specjalność: Drogowa Nr uprawnień: POM/0173/POOD/06	Podpis:
Projektant:	mgr inż. Mariusz Burakowski	Specjalność: Sanitarna Nr uprawnień: Bł/194/01	Podpis:
Projektant:	mgr inż. Aleksandra Koelmer	Specjalność: Sanitarna Nr uprawnień: POM/0463/PWBS/21	Podpis:
Sprawdzający:	mgr inż. Agnieszka Gricman	Specjalność: Sanitarna Nr uprawnień: WAM/0082/PBS/20	Podpis:
Opracowujący:	mgr inż. Piotr Wernecki	Specjalność: - Nr uprawnień: -	Podpis:
Opracowujący:	inż. Marta Przysowa	Specjalność: - Nr uprawnień: -	Podpis:

Data:	Branża:	Skala:	Rewizja:	Rysunek:
Kwiecień 2026 r.	SANITARNA	1:100/1:500	03-K00	3.12

OZNACZENIE PROFILU:
POZIOM PORÓWNAWCZY
RZĘDNA TERENU PROJ.
RZĘDNA TERENU ISTN.
RZĘDNA DNA KANAŁU
ZAGŁĘBIENIE DNA KANAŁU
SPADKI, DŁUGOŚCI
ŚREDNICA, MATERIAŁ
ODLEGŁOŚCI
HEKTOMETRY
Ø200
ściek sk.
P.S.I.EPI-Graf, Generator rysunkowy Profili Koordynator 8.0

Oznaczenia:

🟩	Teren istniejący
🟧	Teren projektowany

Inwestor:

GDDKiA

Skarb Państwa - Generalny Dyrektor Dróg Krajowych i Autostrad z siedzibą w Warszawie ul. Wronia 53, 00-874 Warszawa reprezentowany przez GDDKiA Oddział w Zielonej Górze ul. Boh. Westerplatte 31, 65-950 Zielona Góra

Wykonawca:

POLAQUA POLAQUA Sp.z.o.o.
05-500 Piaseczno,
Wólka Kozodawska ul. Dworcowa 1

Jednostka projektowa:

Highway Sp. z o.o.
80-175 Gdańsk, ul. Jabłoniowa 20
tel./fax. 58 710 05 93
biuro@hwy.com.pl www.hwy.com.pl

Zadanie:

"Budowa obwodnicy miejscowości Krosno Odrzańskie w ciągu drogi krajowej nr 29"

Stadium:	PROJEKT WYKONAWCZY		
Treść rysunku:	Profile kanalizacji deszczowej		
Główny projektant:	mgr inż. Piotr Urbański	Specjalność: Drogowa Nr uprawnień: POM/0173/POOD/06	Podpis:
Projektant:	mgr inż. Mariusz Burakowski	Specjalność: Sanitarna Nr uprawnień: Bl/194/01	Podpis:
Projektant:	mgr inż. Aleksandra Koelmer	Specjalność: Sanitarna Nr uprawnień: POM/0463/PWBS/21	Podpis:
Sprawdzający:	mgr inż. Agnieszka Gricman	Specjalność: Sanitarna Nr uprawnień: WAM/0082/PBS/20	Podpis:
Opracowujący:	mgr inż. Piotr Wernecki	Specjalność: - Nr uprawnień: -	Podpis:
Opracowujący:	inż. Marta Przysowa	Specjalność: - Nr uprawnień: -	Podpis:

Data:	Branża:	Skala:	Rewizja:	Rysunek:
Kwiecień 2026 r.	SANITARNA	1:100/1:500	03-K00	3.13